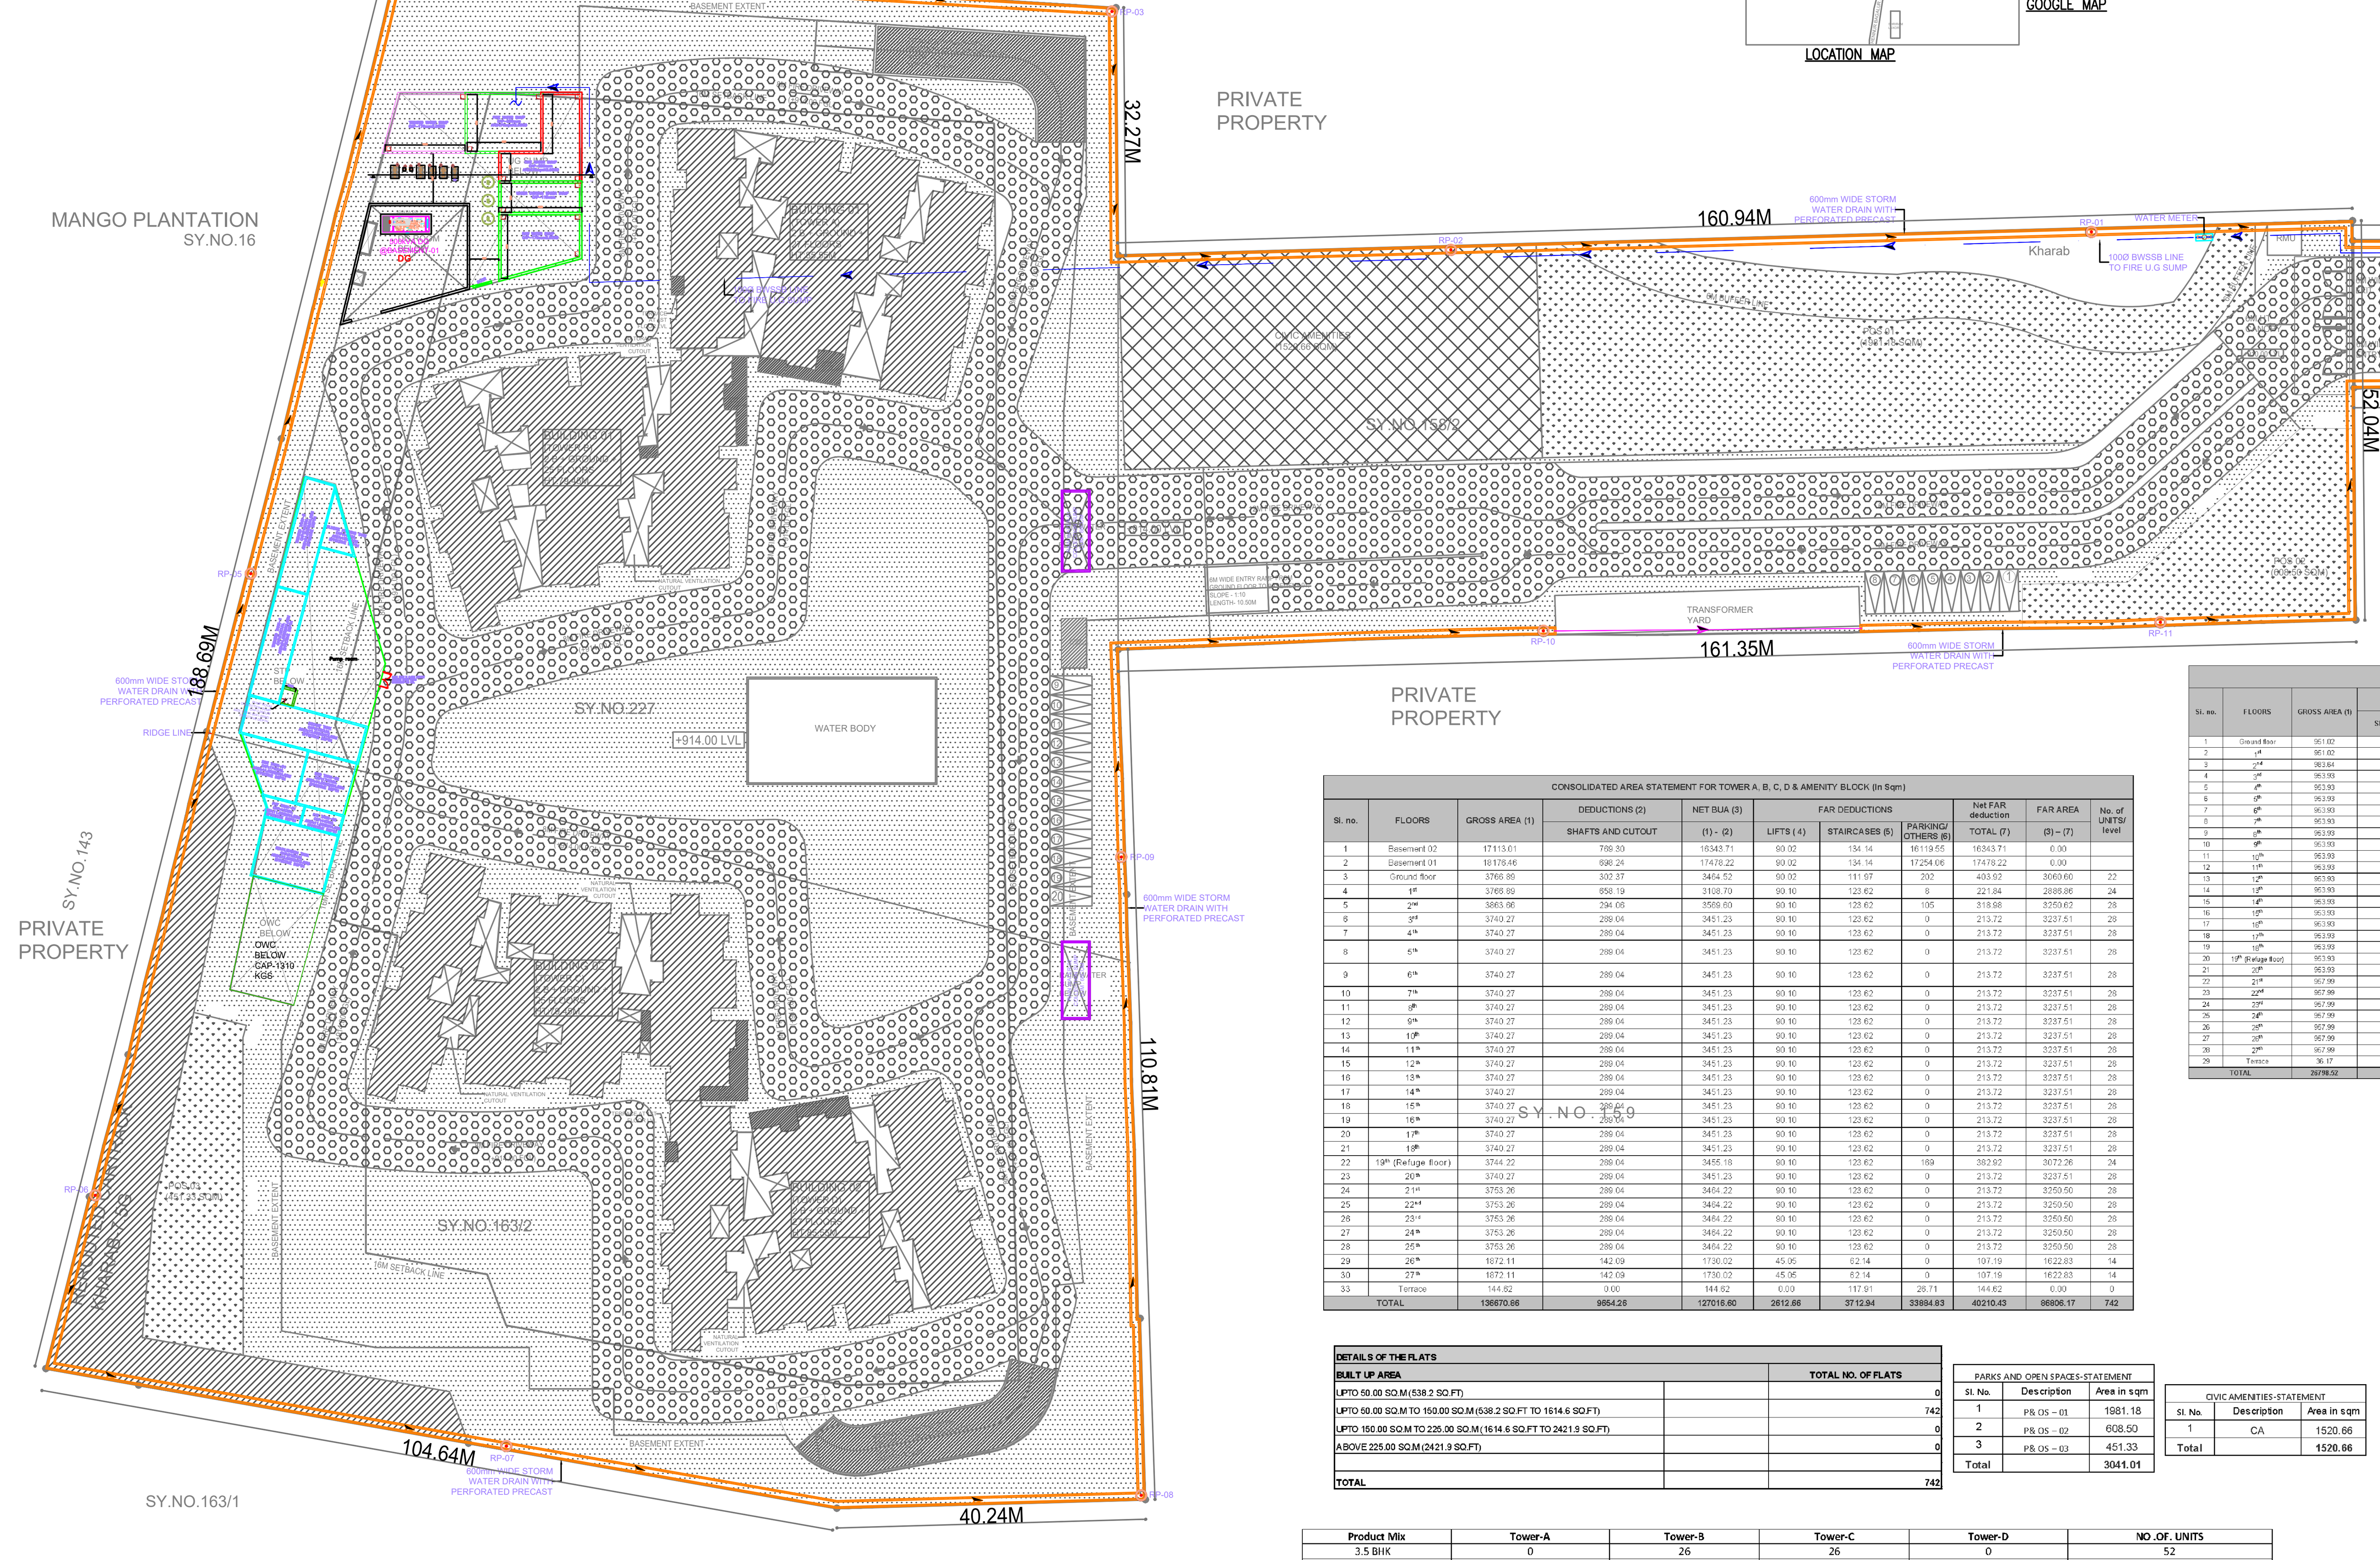
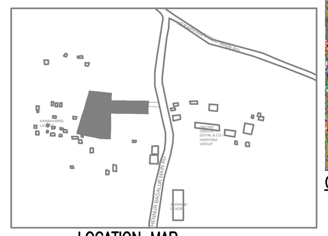
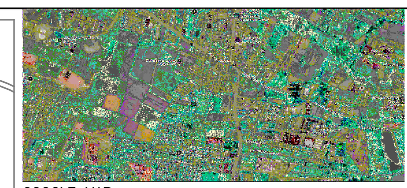



**AREA STATEMENT FOR TOWER D (In Sqm.)**

| Si. no. | FLOORS | GROSS AREA (1) | DEDUCTIONS (2) SHAFTS AND CUTOUT | NET BUA (3) (1) - (2) | FAR DEDUCTIONS LIFTS (4) | FAR DEDUCTIONS STAIRCASES (5) | FAR DEDUCTIONS PARKING/ OTHERS (6) | Net FAR deduction TOTAL (7) | FAR AREA (3) – (7) | No. of UNITS/ level |
|---|---|---|---|---|---|---|---|---|---|---|
| 1 | Ground floor | 951.02 | 77.47 | 873.55 | 22.88 | 27.74 | 104.96 | 155.58 | 717.97 | 5 |
| 2 | 1st | 951.02 | 155.92 | 795.10 | 22.88 | 30.87 | 4.22 | 57.97 | 737.13 | 6 |
| 3 | 2nd | 983.64 | 76.15 | 907.49 | 22.88 | 30.87 | 16.59 | 70.34 | 837.15 | 7 |
| 4 | 3rd | 953.93 | 76.15 | 877.78 | 22.88 | 30.87 | 0.00 | 53.75 | 824.03 | 7 |
| 5 | 4th | 953.93 | 76.15 | 877.78 | 22.88 | 30.87 | 0.00 | 53.75 | 824.03 | 7 |
| 6 | 5th | 953.93 | 76.15 | 877.78 | 22.88 | 30.87 | 0.00 | 53.75 | 824.03 | 7 |
| 7 | 6th | 953.93 | 76.15 | 877.78 | 22.88 | 30.87 | 0.00 | 53.75 | 824.03 | 7 |
| 8 | 7th | 953.93 | 76.15 | 877.78 | 22.88 | 30.87 | 0.00 | 53.75 | 824.03 | 7 |
| 9 | 8th | 953.93 | 76.15 | 877.78 | 22.88 | 30.87 | 0.00 | 53.75 | 824.03 | 7 |
| 10 | 9th | 953.93 | 76.15 | 877.78 | 22.88 | 30.87 | 0.00 | 53.75 | 824.03 | 7 |
| 11 | 10th | 953.93 | 76.15 | 877.78 | 22.88 | 30.87 | 0.00 | 53.75 | 824.03 | 7 |
| 12 | 11th | 953.93 | 76.15 | 877.78 | 22.88 | 30.87 | 0.00 | 53.75 | 824.03 | 7 |
| 13 | 12th | 953.93 | 76.15 | 877.78 | 22.88 | 30.87 | 0.00 | 53.75 | 824.03 | 7 |
| 14 | 13th | 953.93 | 76.15 | 877.78 | 22.88 | 30.87 | 0.00 | 53.75 | 824.03 | 7 |
| 15 | 14th | 953.93 | 76.15 | 877.78 | 22.88 | 30.87 | 0.00 | 53.75 | 824.03 | 7 |
| 16 | 15th | 953.93 | 76.15 | 877.78 | 22.88 | 30.87 | 0.00 | 53.75 | 824.03 | 7 |
| 17 | 16th | 953.93 | 76.15 | 877.78 | 22.88 | 30.87 | 0.00 | 53.75 | 824.03 | 7 |
| 18 | 17th | 953.93 | 76.15 | 877.78 | 22.88 | 30.87 | 0.00 | 53.75 | 824.03 | 7 |
| 19 | 18th | 953.93 | 76.15 | 877.78 | 22.88 | 30.87 | 0.00 | 53.75 | 824.03 | 7 |
| 20 | 19th (Refuge floor) | 953.93 | 76.15 | 877.78 | 22.88 | 30.87 | 44.00 | 97.75 | 780.03 | 6 |
| 21 | 20th | 953.93 | 76.15 | 877.78 | 22.88 | 30.87 | 0 | 53.75 | 824.03 | 7 |
| 22 | 21st | 957.99 | 76.15 | 881.84 | 22.88 | 30.87 | 0.00 | 53.75 | 828.09 | 7 |
| 23 | 22nd | 957.99 | 76.15 | 881.84 | 22.88 | 30.87 | 0.00 | 53.75 | 828.09 | 7 |
| 24 | 23rd | 957.99 | 76.15 | 881.84 | 22.88 | 30.87 | 0.00 | 53.75 | 828.09 | 7 |
| 25 | 24th | 957.99 | 76.15 | 881.84 | 22.88 | 30.87 | 0.00 | 53.75 | 828.09 | 7 |
| 26 | 25th | 957.99 | 76.15 | 881.84 | 22.88 | 30.87 | 0.00 | 53.75 | 828.09 | 7 |
| 27 | 26th | 957.99 | 76.15 | 881.84 | 22.88 | 30.87 | 0.00 | 53.75 | 828.09 | 7 |
| 28 | 27th | 957.99 | 76.15 | 881.84 | 22.88 | 30.87 | 0.00 | 53.75 | 828.09 | 7 |
| 29 | Terrace | 36.17 | 0.00 | 36.17 | 0.00 | 29.43 | 6.74 | 36.17 | 0.00 | 0 |
| TOTAL | | 26798.52 | 2213.29 | 24585.23 | 640.64 | 890.66 | 176.51 | 1707.81 | 22877.42 | 192 |

**CONSOLIDATED AREA STATEMENT FOR TOWER A, B, C, D & AMENITY BLOCK (In Sqm)**

| Si. no. | FLOORS | GROSS AREA (1) | DEDUCTIONS (2) SHAFTS AND CUTOUT | NET BUA (3) (1) - (2) | FAR DEDUCTIONS LIFTS (4) | FAR DEDUCTIONS STAIRCASES (5) | FAR DEDUCTIONS PARKING/ OTHERS (6) | Net FAR deduction TOTAL (7) | FAR AREA (3) – (7) | No. of UNITS/ level |
|---|---|---|---|---|---|---|---|---|---|---|
| 1 | Basement 02 | 17113.01 | 769.30 | 16343.71 | 90.02 | 134.14 | 16119.55 | 16343.71 | 0.00 | |
| 2 | Basement 01 | 18176.46 | 698.24 | 17478.22 | 90.02 | 134.14 | 17254.06 | 17478.22 | 0.00 | |
| 3 | Ground floor | 3766.89 | 302.37 | 3464.52 | 90.02 | 111.97 | 202 | 403.92 | 3060.60 | 22 |
| 4 | 1st | 3766.89 | 658.19 | 3108.70 | 90.10 | 123.62 | 8 | 221.84 | 2886.86 | 24 |
| 5 | 2nd | 3863.66 | 294.06 | 3569.60 | 90.10 | 123.62 | 105 | 318.98 | 3250.62 | 28 |
| 6 | 3rd | 3740.27 | 289.04 | 3451.23 | 90.10 | 123.62 | 0 | 213.72 | 3237.51 | 28 |
| 7 | 4th | 3740.27 | 289.04 | 3451.23 | 90.10 | 123.62 | 0 | 213.72 | 3237.51 | 28 |
| 8 | 5th | 3740.27 | 289.04 | 3451.23 | 90.10 | 123.62 | 0 | 213.72 | 3237.51 | 28 |
| 9 | 6th | 3740.27 | 289.04 | 3451.23 | 90.10 | 123.62 | 0 | 213.72 | 3237.51 | 28 |
| 10 | 7th | 3740.27 | 289.04 | 3451.23 | 90.10 | 123.62 | 0 | 213.72 | 3237.51 | 28 |
| 11 | 8th | 3740.27 | 289.04 | 3451.23 | 90.10 | 123.62 | 0 | 213.72 | 3237.51 | 28 |
| 12 | 9th | 3740.27 | 289.04 | 3451.23 | 90.10 | 123.62 | 0 | 213.72 | 3237.51 | 28 |
| 13 | 10th | 3740.27 | 289.04 | 3451.23 | 90.10 | 123.62 | 0 | 213.72 | 3237.51 | 28 |
| 14 | 11th | 3740.27 | 289.04 | 3451.23 | 90.10 | 123.62 | 0 | 213.72 | 3237.51 | 28 |
| 15 | 12th | 3740.27 | 289.04 | 3451.23 | 90.10 | 123.62 | 0 | 213.72 | 3237.51 | 28 |
| 16 | 13th | 3740.27 | 289.04 | 3451.23 | 90.10 | 123.62 | 0 | 213.72 | 3237.51 | 28 |
| 17 | 14th | 3740.27 | 289.04 | 3451.23 | 90.10 | 123.62 | 0 | 213.72 | 3237.51 | 28 |
| 18 | 15th | 3740.27 | 289.04 | 3451.23 | 90.10 | 123.62 | 0 | 213.72 | 3237.51 | 28 |
| 19 | 16th | 3740.27 | 289.04 | 3451.23 | 90.10 | 123.62 | 0 | 213.72 | 3237.51 | 28 |
| 20 | 17th | 3740.27 | 289.04 | 3451.23 | 90.10 | 123.62 | 0 | 213.72 | 3237.51 | 28 |
| 21 | 18th | 3740.27 | 289.04 | 3451.23 | 90.10 | 123.62 | 0 | 213.72 | 3237.51 | 28 |
| 22 | 19th (Refuge floor) | 3744.22 | 289.04 | 3455.18 | 90.10 | 123.62 | 169 | 382.92 | 3072.26 | 24 |
| 23 | 20th | 3740.27 | 289.04 | 3451.23 | 90.10 | 123.62 | 0 | 213.72 | 3237.51 | 28 |
| 24 | 21st | 3753.26 | 289.04 | 3464.22 | 90.10 | 123.62 | 0 | 213.72 | 3250.50 | 28 |
| 25 | 22nd | 3753.26 | 289.04 | 3464.22 | 90.10 | 123.62 | 0 | 213.72 | 3250.50 | 28 |
| 26 | 23rd | 3753.26 | 289.04 | 3464.22 | 90.10 | 123.62 | 0 | 213.72 | 3250.50 | 28 |
| 27 | 24th | 3753.26 | 289.04 | 3464.22 | 90.10 | 123.62 | 0 | 213.72 | 3250.50 | 28 |
| 28 | 25th | 3753.26 | 289.04 | 3464.22 | 90.10 | 123.62 | 0 | 213.72 | 3250.50 | 28 |
| 29 | 26th | 1872.11 | 142.09 | 1730.02 | 45.05 | 62.14 | 0 | 107.19 | 1622.83 | 14 |
| 30 | 27th | 1872.11 | 142.09 | 1730.02 | 45.05 | 62.14 | 0 | 107.19 | 1622.83 | 14 |
| 33 | Terrace | 144.62 | 0.00 | 144.62 | 0.00 | 117.91 | 26.71 | 144.62 | 0.00 | 0 |
| TOTAL | | 136670.66 | 9654.26 | 127016.60 | 2612.66 | 3712.94 | 33884.83 | 40210.43 | 86806.17 | 742 |

SY.NO.159

**DETAILS OF THE FLATS**

| BUILT UP AREA | | TOTAL NO. OF FLATS |
|---|---|---|
| UPTO 50.00 SQ.M (538.2 SQ.FT) | | 0 |
| UPTO 50.00 SQ.M TO 150.00 SQ.M (538.2 SQ.FT TO 1614.6 SQ.FT) | | 742 |
| UPTO 150.00 SQ.M TO 225.00 SQ.M (1614.6 SQ.FT TO 2421.9 SQ.FT) | | 0 |
| ABOVE 225.00 SQ.M (2421.9 SQ.FT) | | 0 |
| | | |
| TOTAL | | 742 |


**PARKS AND OPEN SPACES-STATEMENT**


| Sl. No. | Description | Area in sqm |
|---|---|---|
| 1 | P& OS – 01 | 1981.18 |
| 2 | P& OS – 02 | 608.50 |
| 3 | P& OS – 03 | 451.33 |
| Total | | 3041.01 |

**CIVIC AMENITIES-STATEMENT**

| Sl. No. | Description | Area in sqm |
|---|---|---|
| 1 | CA | 1520.66 |
| Total | | 1520.66 |

| Product Mix | Tower-A | Tower-B | Tower-C | Tower-D | NO .OF. UNITS |
|---|---|---|---|---|---|
| 3.5 BHK | 0 | 26 | 26 | 0 | 52 |
| 3 Bhk | 56 | 52 | 52 | 84 | 244 |
| 2.5 BHK | 81 | 50 | 26 | 53 | 210 |
| 2 Bhk | 55 | 51 | 75 | 55 | 236 |
| Total units | 192 | 179 | 179 | 192 | 742 |

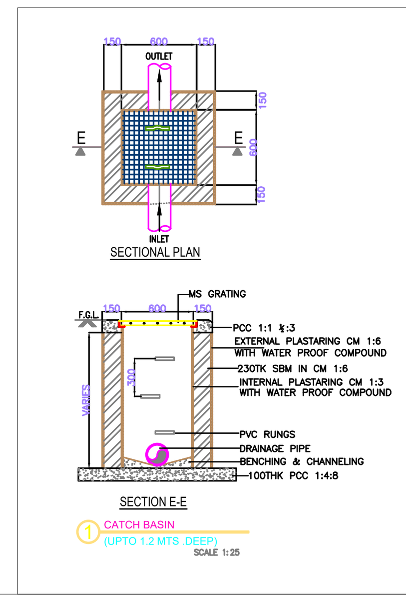

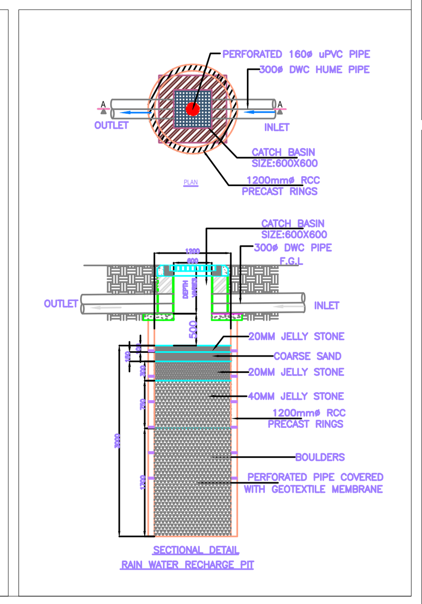
**AREA STATEMENT**

| Sl. No. | Particulars | As Per ZR | As Per Plan | |
|---|---|---|---|---|
| 1 | Land area | | 31,160.53 | SQM |
| 2 | Kharab area | | 758.77 | SQM |
| | | | | |
| 3 | Net site area | | 30,401.76 | SQM |
| | | | | |
| 4 | Area reservations for Parks and Open Spaces | 3040.18<br>10% | 3,041.01<br>10% | SQM |
| | | | | |
| 5 | Area reserved for Civic Amenities | 1520.09<br>5% | 1,520.66<br>10% | SQM |
| | | | | |
| 6 | Area considered for FAR | 28881.67 | | SQM |
| | | | | |
| 7 | Area considered for Ground Coverage | 28881.67 | | SQM |
| | | | | |
| 8 | Permissible FAR area | 3.00 | 86819.27<br>28,881.67 | 3.01 |
| | | | | |
| 9 | Ground Coverage | 50%<br>14440.84 | 3464.52<br>28,881.67 | 12.00% |
| | | | | |
| 10 | Height | | | |
| | Building 01 | | | |
| | Tower A | | 85.55 | m |
| | Tower B | | 79.45 | m |
| | Building 02 | | | |
| | Tower C | | 79.45 | m |
| | Tower D | | 85.55 | m |
| | | | | |
| 11 | Minimum Setbacks | | | |
| | Front | | 16 | m |
| | Rear | | 16 | m |
| | Left | | 16 | m |
| | Right | | 16 | m |
| 12 | No. of Floors | | | |
| | Tower A | | 2B+Ground+27 upper floors | |
| | Tower B | | 2B+Ground+25 upper floors | |
| | Tower C | | 2B+Ground+25 upper floors | |
| | Tower D | | 2B+Ground+27 upper floors | |
| | | | | |
| 13 | No. of units | | 742 | No.s |
| | | | | |
| 14 | Car Parking Statement | | | |
| | No. of units proposed with less than 50 sqm | | | |
| | No. of proposed Units with area more than 50 sqm and less than 224 sqm | | 742 | No.s |
| | Parking required @ 1 car/every unit | | 742 | No.s |
| | Total parking required for units | | 742 | No.s |
| | Visitor parking @10% | 74.2 | 75 | No.s |
| | | | | |
| | Total Parking Requirement for the development | | 817 | No.s |
| | | | | |
| 15 | Parking Provided | | | |
| | Basement 01 | | 443 | No.s |
| | Basement 02 | | 453 | No.s |
| | Surface parking | | 20 | No.s |
| | Total parking provided | | 916 | No.s |

**AREA STATEMENT FOR TOWER A (In Sqm.)**

| Si. no. | FLOORS | GROSS AREA (1) | DEDUCTIONS (2) SHAFTS AND CUTOUT | NET BUA (3) (1) - (2) | FAR DEDUCTIONS LIFTS (4) | FAR DEDUCTIONS STAIRCASES (5) | FAR DEDUCTIONS PARKING/ OTHERS (6) | Net FAR deduction TOTAL (7) | FAR AREA (3) – (7) | No. of UNITS/ level |
|---|---|---|---|---|---|---|---|---|---|---|
| 1 | Ground floor | 914.22 | 73.81 | 840.41 | 22.17 | 27.05 | 87.97 | 137.99 | 702.42 | 5 |
| 2 | 1st | 914.22 | 155.02 | 759.20 | 22.17 | 31.27 | 3.90 | 57.34 | 701.86 | 6 |
| 3 | 2nd | 937.53 | 65.94 | 871.59 | 22.17 | 31.27 | 27.52 | 80.96 | 790.63 | 7 |
| 4 | 3rd | 909.99 | 65.94 | 844.05 | 22.17 | 31.27 | 0 | 53.44 | 790.61 | 7 |
| 5 | 4th | 909.99 | 65.94 | 844.05 | 22.17 | 31.27 | 0 | 53.44 | 790.61 | 7 |
| 6 | 5th | 909.99 | 65.94 | 844.05 | 22.17 | 31.27 | 0 | 53.44 | 790.61 | 7 |
| 7 | 6th | 909.99 | 65.94 | 844.05 | 22.17 | 31.27 | 0 | 53.44 | 790.61 | 7 |
| 8 | 7th | 909.99 | 65.94 | 844.05 | 22.17 | 31.27 | 0 | 53.44 | 790.61 | 7 |
| 9 | 8th | 909.99 | 65.94 | 844.05 | 22.17 | 31.27 | 0 | 53.44 | 790.61 | 7 |
| 10 | 9th | 909.99 | 65.94 | 844.05 | 22.17 | 31.27 | 0 | 53.44 | 790.61 | 7 |
| 11 | 10th | 909.99 | 65.94 | 844.05 | 22.17 | 31.27 | 0 | 53.44 | 790.61 | 7 |
| 12 | 11th | 909.99 | 65.94 | 844.05 | 22.17 | 31.27 | 0 | 53.44 | 790.61 | 7 |
| 13 | 12th | 909.99 | 65.94 | 844.05 | 22.17 | 31.27 | 0 | 53.44 | 790.61 | 7 |
| 14 | 13th | 909.99 | 65.94 | 844.05 | 22.17 | 31.27 | 0 | 53.44 | 790.61 | 7 |
| 15 | 14th | 909.99 | 65.94 | 844.05 | 22.17 | 31.27 | 0 | 53.44 | 790.61 | 7 |
| 16 | 15th | 909.99 | 65.94 | 844.05 | 22.17 | 31.27 | 0 | 53.44 | 790.61 | 7 |
| 17 | 16th | 909.99 | 65.94 | 844.05 | 22.17 | 31.27 | 0 | 53.44 | 790.61 | 7 |
| 18 | 17th | 909.99 | 65.94 | 844.05 | 22.17 | 31.27 | 0 | 53.44 | 790.61 | 7 |
| 19 | 18th | 909.99 | 65.94 | 844.05 | 22.17 | 31.27 | 0 | 53.44 | 790.61 | 7 |
| 20 | 19th (Refuge floor) | 909.99 | 65.94 | 844.05 | 22.17 | 31.27 | 42.2 | 95.64 | 748.41 | 6 |
| 21 | 20th | 909.99 | 65.94 | 844.05 | 22.17 | 31.27 | 0 | 53.44 | 790.61 | 7 |
| 22 | 21st | 914.12 | 65.94 | 848.18 | 22.17 | 31.27 | 0 | 53.44 | 794.74 | 7 |
| 23 | 22nd | 914.12 | 65.94 | 848.18 | 22.17 | 31.27 | 0 | 53.44 | 794.74 | 7 |
| 34 | 23rd | 914.12 | 65.94 | 848.18 | 22.17 | 31.27 | 0 | 53.44 | 794.74 | 7 |
| 25 | 24th | 914.12 | 65.94 | 848.18 | 22.17 | 31.27 | 0 | 53.44 | 794.74 | 7 |
| 26 | 25th | 914.12 | 65.94 | 848.18 | 22.17 | 31.27 | 0 | 53.44 | 794.74 | 7 |
| 27 | 26th | 914.12 | 65.94 | 848.18 | 22.17 | 31.27 | 0 | 53.44 | 794.74 | 7 |
| 28 | 27th | 914.12 | 65.94 | 848.18 | 22.17 | 31.27 | 0 | 53.44 | 794.74 | 7 |
| 29 | Terrace | 36.31 | 0.00 | 36.31 | 0.00 | 29.80 | 6.51 | 36.31 | 0.00 | 0 |
| TOTAL | | 25580.94 | 1943.27 | 23637.67 | 620.76 | 901.94 | 168.10 | 1690.80 | 21946.87 | 192 |

**AREA STATEMENT FOR TOWER B (In Sqm.)**


| Si. no. | FLOORS | GROSS AREA (1) | DEDUCTIONS (2) SHAFTS AND CUTOUT | NET BUA (3) (1) - (2) | FAR DEDUCTIONS LIFTS (4) | FAR DEDUCTIONS STAIRCASES (5) | FAR DEDUCTIONS PARKING/ OTHERS (6) | Net FAR deduction TOTAL (7) | FAR AREA (3) – (7) | No. of UNITS/ level |
|---|---|---|---|---|---|---|---|---|---|---|
| 1 | Ground floor | 949.08 | 71.40 | 877.68 | 22.17 | 27.86 | 4.10 | 54.13 | 823.55 | 6 |
| 2 | 1st | 949.08 | 177.86 | 771.22 | 22.17 | 31.27 | 0.00 | 53.44 | 717.78 | 6 |
| 3 | 2nd | 965.87 | 71.38 | 894.49 | 22.17 | 31.27 | 28.39 | 81.83 | 812.66 | 7 |
| 4 | 3rd | 937.54 | 71.38 | 866.16 | 22.17 | 31.27 | 0.00 | 53.44 | 812.72 | 7 |
| 5 | 4th | 937.54 | 71.38 | 866.16 | 22.17 | 31.27 | 0.00 | 53.44 | 812.72 | 7 |
| 6 | 5th | 937.54 | 71.38 | 866.16 | 22.17 | 31.27 | 0.00 | 53.44 | 812.72 | 7 |
| 7 | 6th | 937.54 | 71.38 | 866.16 | 22.17 | 31.27 | 0.00 | 53.44 | 812.72 | 7 |
| 8 | 7th | 937.54 | 71.38 | 866.16 | 22.17 | 31.27 | 0.00 | 53.44 | 812.72 | 7 |
| 9 | 8th | 937.54 | 71.38 | 866.16 | 22.17 | 31.27 | 0.00 | 53.44 | 812.72 | 7 |
| 10 | 9th | 937.54 | 71.38 | 866.16 | 22.17 | 31.27 | 0.00 | 53.44 | 812.72 | 7 |
| 11 | 10th | 937.54 | 71.38 | 866.16 | 22.17 | 31.27 | 0.00 | 53.44 | 812.72 | 7 |
| 12 | 11th | 937.54 | 71.38 | 866.16 | 22.17 | 31.27 | 0.00 | 53.44 | 812.72 | 7 |
| 13 | 12th | 937.54 | 71.38 | 866.16 | 22.17 | 31.27 | 0.00 | 53.44 | 812.72 | 7 |
| 14 | 13th | 937.54 | 71.38 | 866.16 | 22.17 | 31.27 | 0.00 | 53.44 | 812.72 | 7 |
| 15 | 14th | 937.54 | 71.38 | 866.16 | 22.17 | 31.27 | 0.00 | 53.44 | 812.72 | 7 |
| 16 | 15th | 937.54 | 71.38 | 866.16 | 22.17 | 31.27 | 0.00 | 53.44 | 812.72 | 7 |
| 17 | 16th | 937.54 | 71.38 | 866.16 | 22.17 | 31.27 | 0.00 | 53.44 | 812.72 | 7 |
| 18 | 17th | 937.54 | 71.38 | 866.16 | 22.17 | 31.27 | 0.00 | 53.44 | 812.72 | 7 |
| 19 | 18th | 937.54 | 71.38 | 866.16 | 22.17 | 31.27 | 0.00 | 53.44 | 812.72 | 7 |
| 20 | 19th (Refuge floor) | 937.54 | 71.38 | 866.16 | 22.17 | 31.27 | 43.40 | 96.84 | 769.32 | 6 |
| 21 | 20th | 937.54 | 71.38 | 866.16 | 22.17 | 31.27 | 0.00 | 53.44 | 812.72 | 7 |
| 22 | 21st | 942.43 | 71.38 | 871.05 | 22.17 | 31.27 | 0.00 | 53.44 | 817.61 | 7 |
| 23 | 22nd | 942.43 | 71.38 | 871.05 | 22.17 | 31.27 | 0.00 | 53.44 | 817.61 | 7 |
| 34 | 23rd | 942.43 | 71.38 | 871.05 | 22.17 | 31.27 | 0.00 | 53.44 | 817.61 | 7 |
| 25 | 24th | 942.43 | 71.38 | 871.05 | 22.17 | 31.27 | 0.00 | 53.44 | 817.61 | 7 |
| 26 | 25th | 942.43 | 71.38 | 871.05 | 22.17 | 31.27 | 0.00 | 53.44 | 817.61 | 7 |
| 27 | Terrace | 36.30 | 0.00 | 36.30 | 0.00 | 29.56 | 6.74 | 36.30 | 0.00 | 0 |
| TOTAL | | 24488.20 | 1962.38 | 22525.82 | 576.42 | 839.17 | 82.63 | 1498.22 | 21027.60 | 179 |

**AREA STATEMENT FOR TOWER C (In Sqm.)**


| Si. no. | FLOORS | GROSS AREA (1) | DEDUCTIONS (2) SHAFTS AND CUTOUT | NET BUA (3) (1) - (2) | FAR DEDUCTIONS LIFTS (4) | FAR DEDUCTIONS STAIRCASES (5) | FAR DEDUCTIONS PARKING/ OTHERS (6) | Net FAR deduction TOTAL (7) | FAR AREA (3) – (7) | No. of UNITS/ level |
|---|---|---|---|---|---|---|---|---|---|---|
| 1 | Ground floor | 952.57 | 79.69 | 872.88 | 22.80 | 28.52 | 5 | 56.22 | 816.66 | 6 |
| 2 | 1st | 952.57 | 169.39 | 783.18 | 22.88 | 30.21 | 0 | 53.09 | 730.09 | 6 |
| 3 | 2nd | 976.62 | 80.59 | 896.03 | 22.88 | 30.21 | 32.76 | 85.85 | 810.18 | 7 |
| 4 | 3rd | 938.81 | 75.57 | 863.24 | 22.88 | 30.21 | 0 | 53.09 | 810.15 | 7 |
| 5 | 4th | 938.81 | 75.57 | 863.24 | 22.88 | 30.21 | 0 | 53.09 | 810.15 | 7 |
| 6 | 5th | 938.81 | 75.57 | 863.24 | 22.88 | 30.21 | 0 | 53.09 | 810.15 | 7 |
| 7 | 6th | 938.81 | 75.57 | 863.24 | 22.88 | 30.21 | 0 | 53.09 | 810.15 | 7 |
| 8 | 7th | 938.81 | 75.57 | 863.24 | 22.88 | 30.21 | 0 | 53.09 | 810.15 | 7 |
| 9 | 8th | 938.81 | 75.57 | 863.24 | 22.88 | 30.21 | 0 | 53.09 | 810.15 | 7 |
| 10 | 9th | 938.81 | 75.57 | 863.24 | 22.88 | 30.21 | 0 | 53.09 | 810.15 | 7 |
| 11 | 10th | 938.81 | 75.57 | 863.24 | 22.88 | 30.21 | 0 | 53.09 | 810.15 | 7 |
| 12 | 11th | 938.81 | 75.57 | 863.24 | 22.88 | 30.21 | 0 | 53.09 | 810.15 | 7 |
| 13 | 12th | 938.81 | 75.57 | 863.24 | 22.88 | 30.21 | 0 | 53.09 | 810.15 | 7 |
| 14 | 13th | 938.81 | 75.57 | 863.24 | 22.88 | 30.21 | 0 | 53.09 | 810.15 | 7 |
| 15 | 14th | 938.81 | 75.57 | 863.24 | 22.88 | 30.21 | 0 | 53.09 | 810.15 | 7 |
| 16 | 15th | 938.81 | 75.57 | 863.24 | 22.88 | 30.21 | 0 | 53.09 | 810.15 | 7 |
| 17 | 16th | 938.81 | 75.57 | 863.24 | 22.88 | 30.21 | 0 | 53.09 | 810.15 | 7 |
| 18 | 17th | 938.81 | 75.57 | 863.24 | 22.88 | 30.21 | 0 | 53.09 | 810.15 | 7 |
| 19 | 18th | 938.81 | 75.57 | 863.24 | 22.88 | 30.21 | 0 | 53.09 | 810.15 | 7 |
| 20 | 19th (Refuge floor) | 938.81 | 75.57 | 863.24 | 22.88 | 30.21 | 42.8 | 95.89 | 767.35 | 6 |
| 21 | 20th | 938.81 | 75.57 | 863.24 | 22.88 | 30.21 | 0 | 53.09 | 810.15 | 7 |
| 22 | 21st | 942.77 | 75.57 | 867.20 | 22.88 | 30.21 | 0 | 53.09 | 814.11 | 7 |
| 23 | 22nd | 942.77 | 75.57 | 867.20 | 22.88 | 30.21 | 0 | 53.09 | 814.11 | 7 |
| 24 | 23rd | 942.77 | 75.57 | 867.20 | 22.88 | 30.21 | 0 | 53.09 | 814.11 | 7 |
| 25 | 24th | 942.77 | 75.57 | 867.20 | 22.88 | 30.21 | 0 | 53.09 | 814.11 | 7 |
| 26 | 25th | 942.77 | 75.57 | 867.20 | 22.88 | 30.21 | 0 | 53.09 | 814.11 | 7 |
| 27 | Terrace | 35.84 | 0.00 | 35.84 | 0.00 | 29.12 | 6.72 | 35.84 | 0.00 | 0 |
| TOTAL | | 24530.03 | 2067.78 | 22462.25 | 594.80 | 812.89 | 87.18 | 1494.87 | 20967.38 | 179 |

**CONSOLIDATED AREA STATEMENT FOR TOWER A, B, C, D & AMENITY BLOCK (In Sqm)**


| Si. no. | FLOORS | GROSS AREA (1) | DEDUCTIONS (2) SHAFTS AND CUTOUT | NET BUA (3) (1) - (2) | FAR DEDUCTIONS LIFTS (4) | FAR DEDUCTIONS STAIRCASES (5) | FAR DEDUCTIONS PARKING/ OTHERS (6) | Net FAR deduction TOTAL (7) | FAR AREA (3) – (7) | No. of UNITS/ level |
|---|---|---|---|---|---|---|---|---|---|---|
| 1 | Basement 02 | 17113.01 | 769.30 | 16343.71 | 90.02 | 134.14 | 16119.55 | 16343.71 | 0.00 | |
| 2 | Basement 01 | 18176.46 | 698.24 | 17478.22 | 90.02 | 134.14 | 17254.06 | 17478.22 | 0.00 | |
| 3 | Ground floor | 3766.89 | 302.37 | 3464.52 | 90.02 | 111.97 | 202 | 403.92 | 3060.60 | 22 |
| 4 | 1st | 3766.89 | 658.19 | 3108.70 | 90.10 | 123.62 | 8 | 221.84 | 2886.86 | 24 |
| 5 | 2nd | 3863.66 | 294.06 | 3569.60 | 90.10 | 123.62 | 105 | 318.98 | 3250.62 | 28 |
| 6 | 3rd | 3740.27 | 289.04 | 3451.23 | 90.10 | 123.62 | 0 | 213.72 | 3237.51 | 28 |
| 7 | 4th | 3740.27 | 289.04 | 3451.23 | 90.10 | 123.62 | 0 | 213.72 | 3237.51 | 28 |
| 8 | 5th | 3740.27 | 289.04 | 3451.23 | 90.10 | 123.62 | 0 | 213.72 | 3237.51 | 28 |
| 9 | 6th | 3740.27 | 289.04 | 3451.23 | 90.10 | 123.62 | 0 | 213.72 | 3237.51 | 28 |
| 10 | 7th | 3740.27 | 289.04 | 3451.23 | 90.10 | 123.62 | 0 | 213.72 | 3237.51 | 28 |
| 11 | 8th | 3740.27 | 289.04 | 3451.23 | 90.10 | 123.62 | 0 | 213.72 | 3237.51 | 28 |
| 12 | 9th | 3740.27 | 289.04 | 3451.23 | 90.10 | 123.62 | 0 | 213.72 | 3237.51 | 28 |
| 13 | 10th | 3740.27 | 289.04 | 3451.23 | 90.10 | 123.62 | 0 | 213.72 | 3237.51 | 28 |
| 14 | 11th | 3740.27 | 289.04 | 3451.23 | 90.10 | 123.62 | 0 | 213.72 | 3237.51 | 28 |
| 15 | 12th | 3740.27 | 289.04 | 3451.23 | 90.10 | 123.62 | 0 | 213.72 | 3237.51 | 28 |
| 16 | 13th | 3740.27 | 289.04 | 3451.23 | 90.10 | 123.62 | 0 | 213.72 | 3237.51 | 28 |
| 17 | 14th | 3740.27 | 289.04 | 3451.23 | 90.10 | 123.62 | 0 | 213.72 | 3237.51 | 28 |
| 18 | 15th | 3740.27 | 289.04 | 3451.23 | 90.10 | 123.62 | 0 | 213.72 | 3237.51 | 28 |
| 19 | 16th | 3740.27 | 289.04 | 3451.23 | 90.10 | 123.62 | 0 | 213.72 | 3237.51 | 28 |
| 20 | 17th | 3740.27 | 289.04 | 3451.23 | 90.10 | 123.62 | 0 | 213.72 | 3237.51 | 28 |
| 21 | 18th | 3740.27 | 289.04 | 3451.23 | 90.10 | 123.62 | 0 | 213.72 | 3237.51 | 28 |
| 22 | 19th (Refuge floor) | 3740.27 | 289.04 | 3451.23 | 90.10 | 123.62 | 172 | 386.12 | 3065.11 | 24 |
| 23 | 20th | 3740.27 | 289.04 | 3451.23 | 90.10 | 123.62 | 0 | 213.72 | 3237.51 | 28 |
| 24 | 21st | 3757.31 | 289.04 | 3468.27 | 90.10 | 123.62 | 0 | 213.72 | 3254.55 | 28 |
| 25 | 22nd | 3757.31 | 289.04 | 3468.27 | 90.10 | 123.62 | 0 | 213.72 | 3254.55 | 28 |
| 26 | 23rd | 3757.31 | 289.04 | 3468.27 | 90.10 | 123.62 | 0 | 213.72 | 3254.55 | 28 |
| 27 | 24th | 3757.31 | 289.04 | 3468.27 | 90.10 | 123.62 | 0 | 213.72 | 3254.55 | 28 |
| 28 | 25th | 3757.31 | 289.04 | 3468.27 | 90.10 | 123.62 | 0 | 213.72 | 3254.55 | 28 |
| 29 | 26th | 1872.11 | 142.09 | 1730.02 | 45.05 | 62.14 | 0 | 107.19 | 1622.83 | 14 |
| 30 | 27th | 1872.11 | 142.09 | 1730.02 | 45.05 | 62.14 | 0 | 107.19 | 1622.83 | 14 |
| 33 | Terrace | 144.62 | 0.00 | 144.62 | 0.00 | 117.91 | 26.71 | 144.62 | 0.00 | 0 |
| TOTAL | | 136687.16 | 9654.26 | 127032.90 | 2612.66 | 3712.94 | 33888.03 | 40213.63 | 86819.27 | 742 |

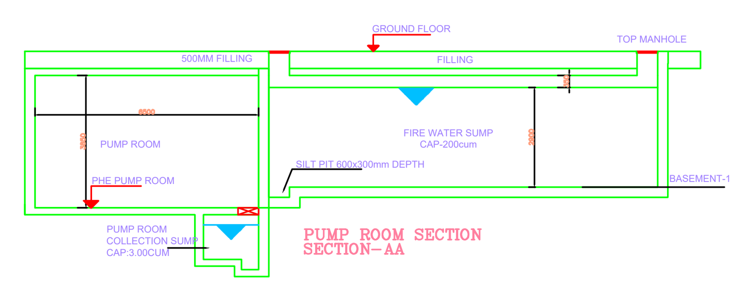



PUMP ROOM SECTION
SECTION– AA

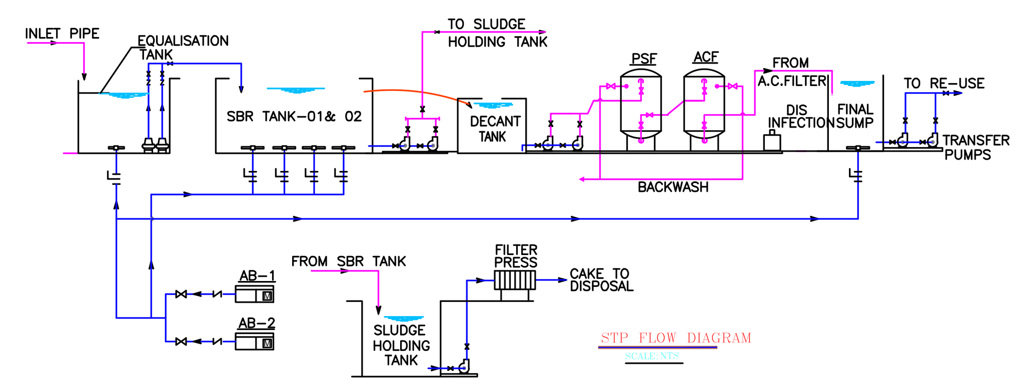



STP FLOW DIAGRAM

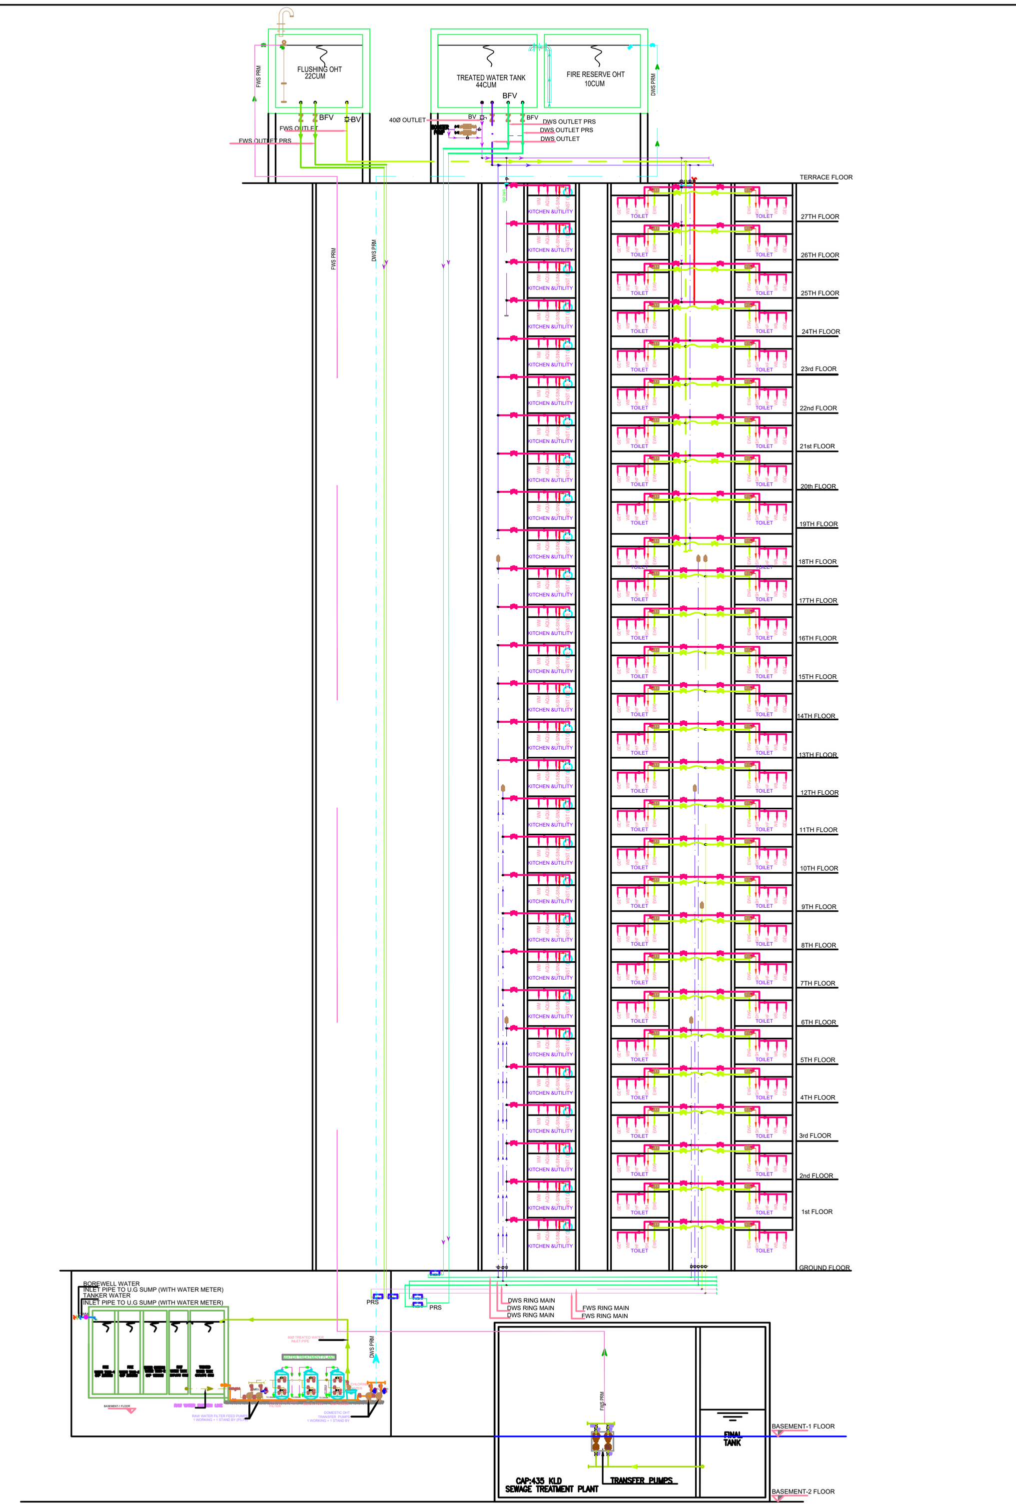

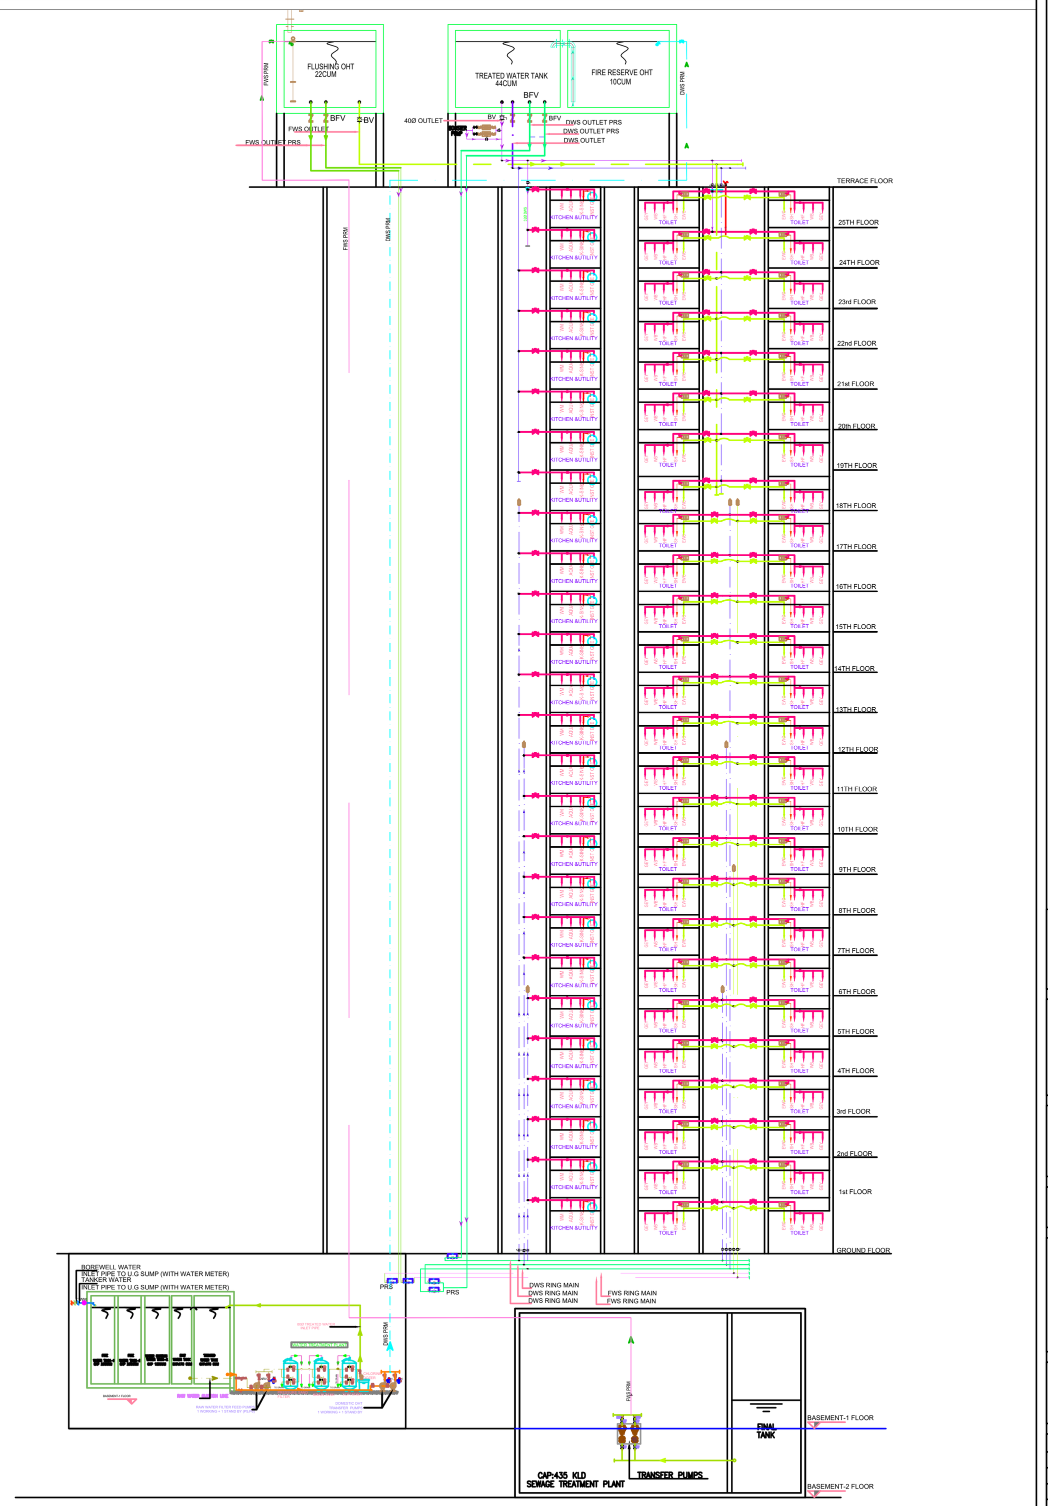
NOTE:-
All information contained in this document are confidential and copyright there of is reserved by MAPLE ENGG DESIGN SERVICES INDIA PVT LTD or any purpose other then for which they are supplied and shall not be copied or reproduced without written permission.

## LOCATION PLAN

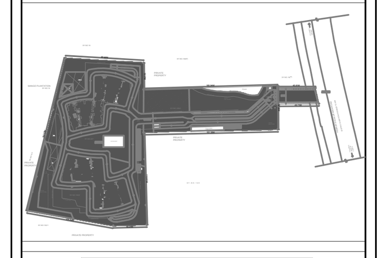

**LEGEND**

| | |
|---|---|
| EWC | EUROPEAN WATER CLOSET WITH CISTERN |
| WB | WASH BASIN |
| HF | HEALTH FAUCET |
| SH | SHOWER |
| SINK | KITCHEN SINK |
| AQ | AQUAGUARD |
| GEY | GEYSER |
| FWS | FLUSHING WATER SUPPLY |
| DWS | DOMESTIC WATER SUPPLY |
| HWS | HOT WATER SUPPLY |

**LEGEND**

| | |
|---|---|
| RP | DEEP RECHARGE PIT |
| | RCC HUME PIPE |
| | BWSSB WATER SUPPLY LINE |
| | FLOW DIRECTION |
| OWC | ORGANIC WASTE CONVERTER |
| BRP | BOREWELL RECHARGE PIT |

PROJECT:
PROPOSED RESIDENTIAL DEVELOPMENT at sy no 227,158/2,163/2,16(P) OF KANNUR VILLAGE,BIDARAHALLI HOBLI, BANGALORE EAST TALUK BANGALORE URBAN DISTRICT

OWNER'S/ AUTHORISED SIGNATURE:
Goyal Hariyana Developers
No.206, Barton Centre, 84 M G Road, Bangalore-560001.

ARCHITECTS' SIGNATURE & LICENCE NO:

Venkataramanan Associates

MAPLE
Maple House, NO.597, 3rd & 4th Floor,
15th Cross Road, Ring Road,JP Nagara 6th Phase,
Bangalore-560078 (INDIA)
Tel: 080-42068194, 22449333, 41211873, 41211872

SITE PLAN
MOEF SANCTION DRAWING

N

| PROJECT NAME: | | | |
|---|---|---|---|
| DRAWN\CHECKED : BHARATH N | DATE : 12.08.2026 | REV | |
| DESIGNED : SCS | SCALE : NTS | R0 | |
| APPROVED : SLP | SHEET : 01 OF 01 | | |
| JOB No : | DRAWING No : MEDS-GK-MOEF-01 | | |